




Light circuit

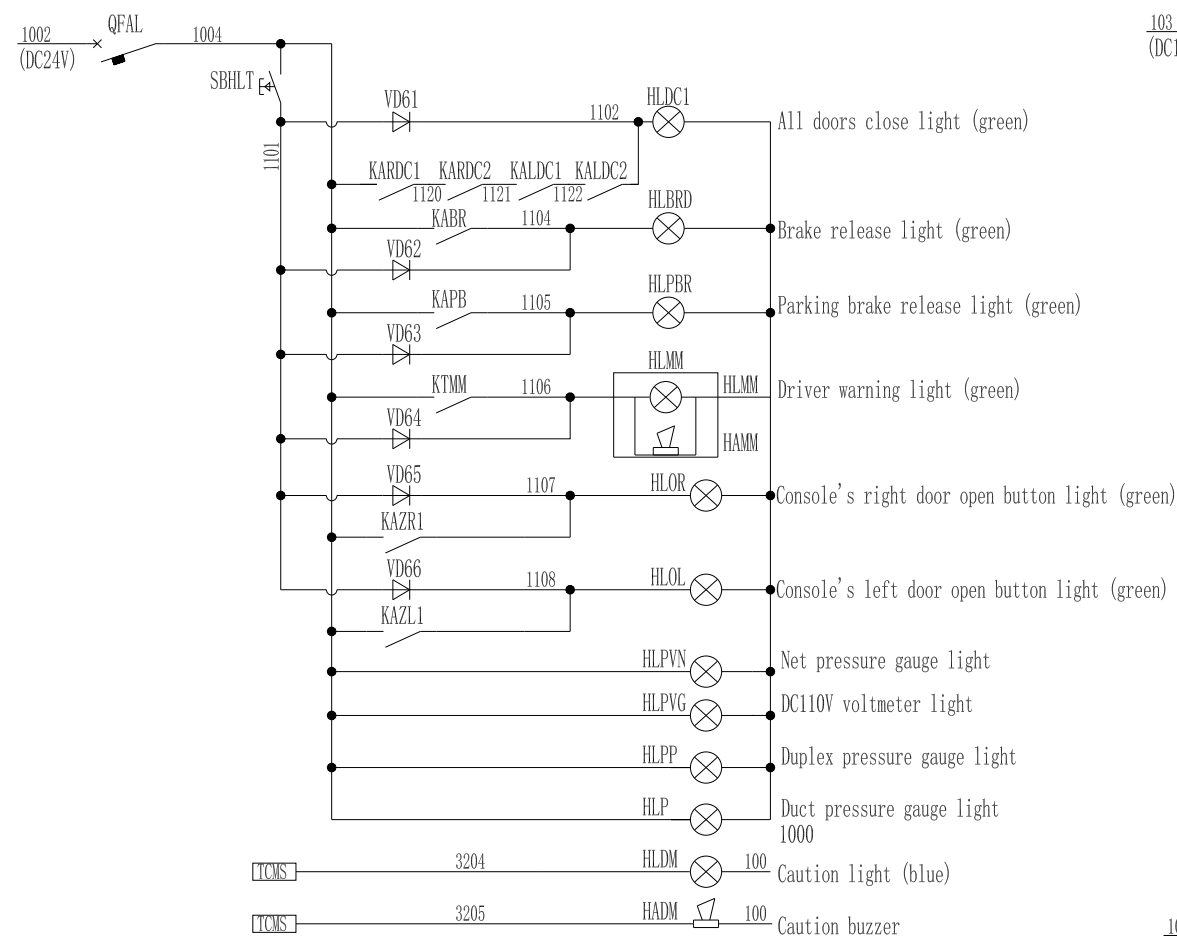


Cab wiper

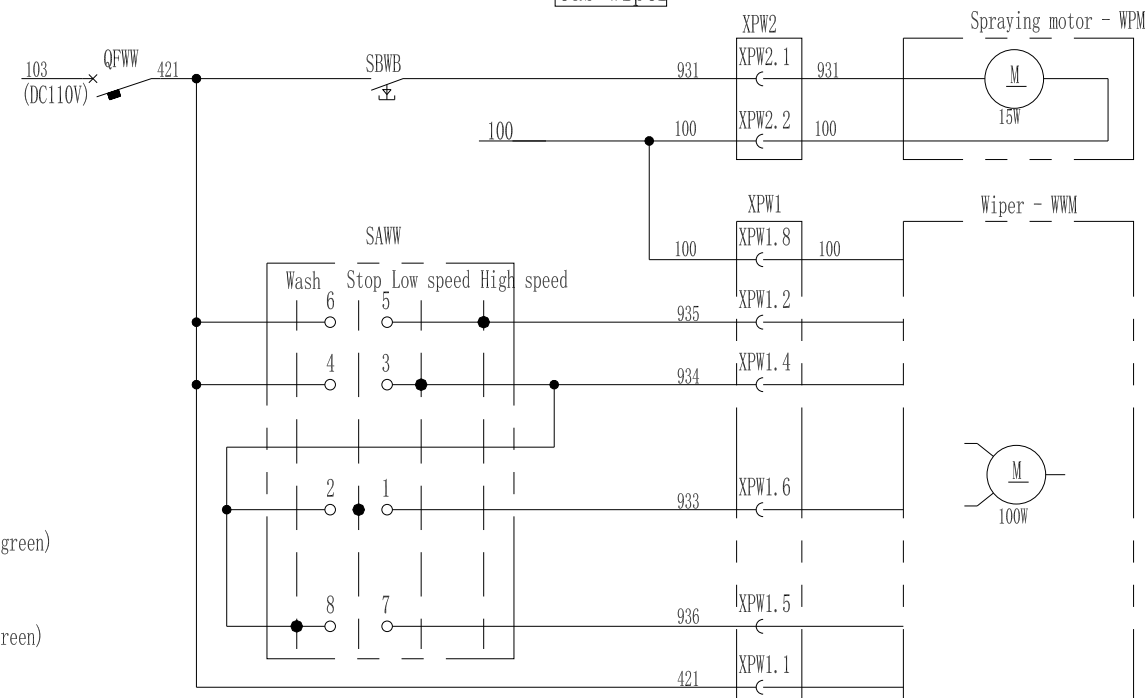

Cab electric heating, electric whistle control

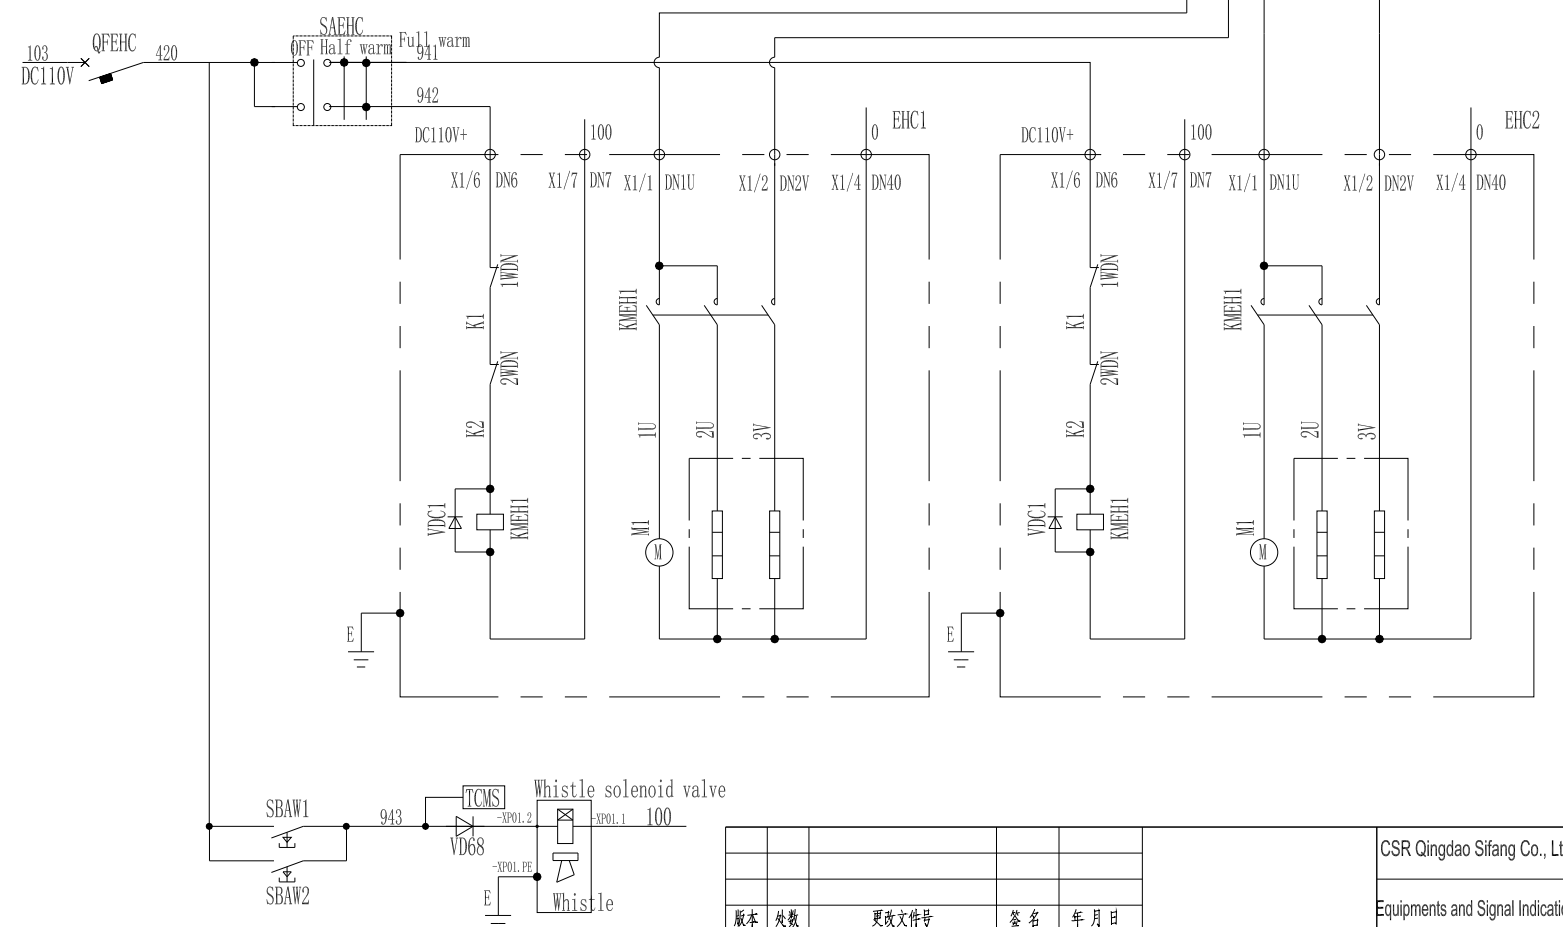

Electrically heated glass control

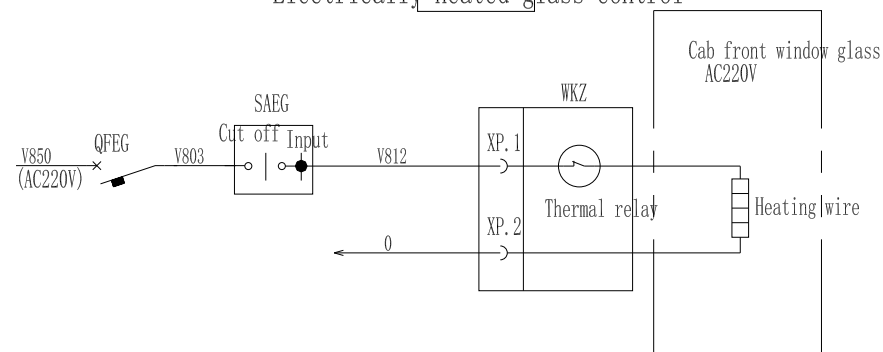

--	--	